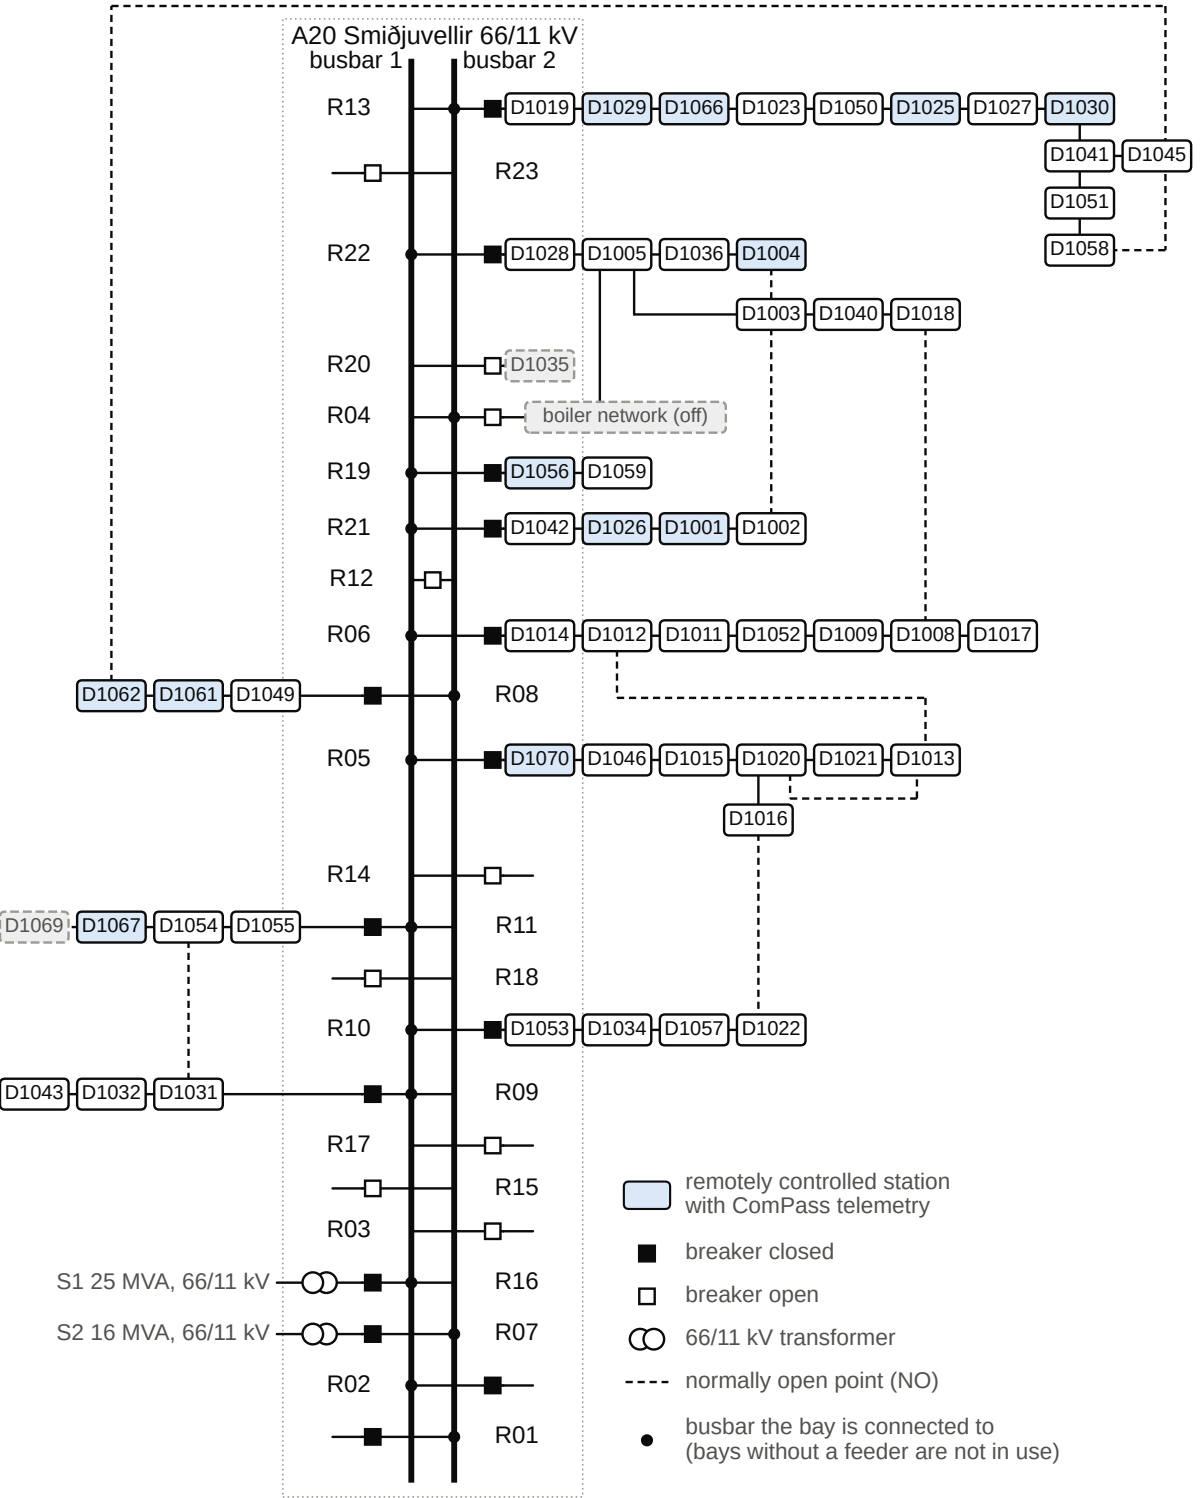
A20 Smiðjuvellir 66/11 kV
busbar 1
busbar 2
R13
R23
R22
R20
R04
R19
R21
R12
R06
R08
R05
R14
R11
R18
R10
R09
R17
R15
R03
R16
R07
R02
R01
D1019
D1029
D1066
D1023
D1050
D1025
D1027
D1030
D1041
D1045
D1051
D1058
D1028
D1005
D1036
D1004
D1003
D1040
D1018
D1035
boiler network (off)
D1056
D1059
D1042
D1026
D1001
D1002
D1014
D1012
D1011
D1052
D1009
D1008
D1017
D1062
D1061
D1049
D1070
D1046
D1015
D1020
D1021
D1013
D1016
D1069
D1067
D1054
D1055
D1053
D1034
D1057
D1022
D1043
D1032
D1031
S1 25 MVA, 66/11 kV
S2 16 MVA, 66/11 kV
remotely controlled station with ComPass telemetry
breaker closed
breaker open
66/11 kV transformer
normally open point (NO)
busbar the bay is connected to (bays without a feeder are not in use)